REV.	DESCRIPTION	DATE	BY	APP'D.
A	REDRAWN & REPLACED	10/93	dak	RW

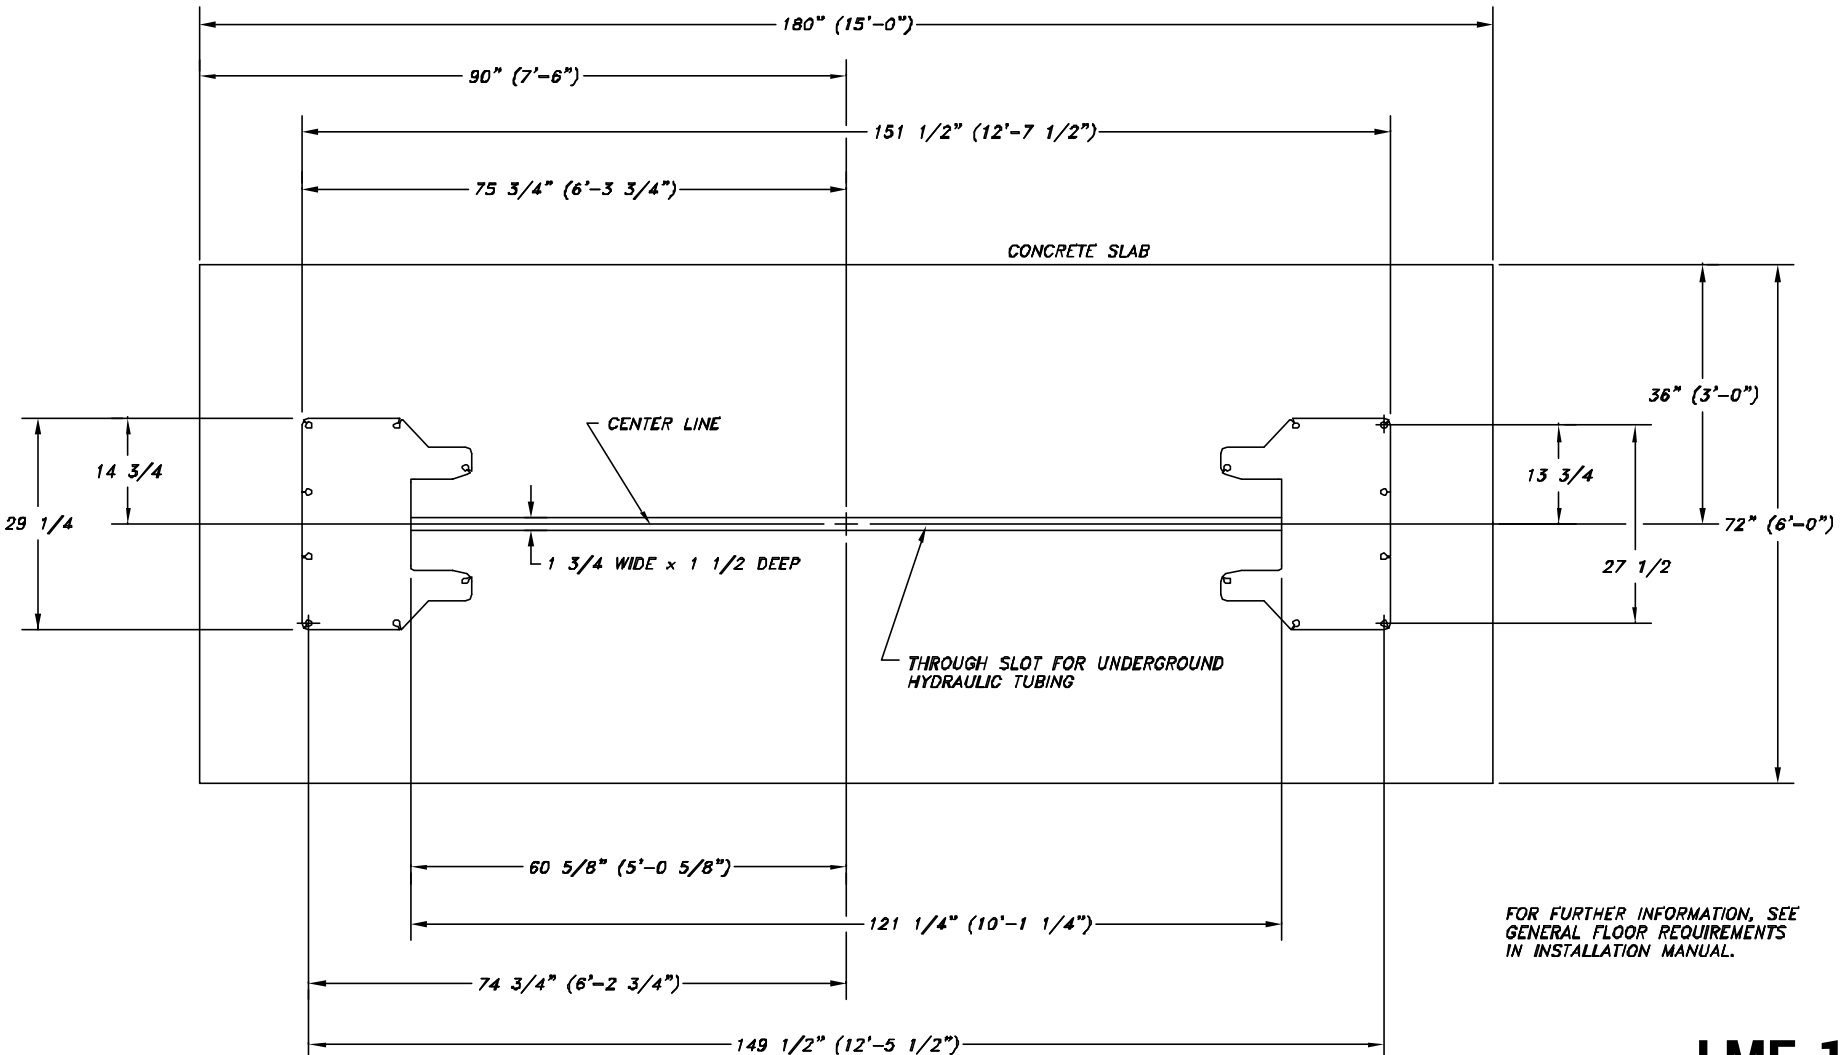

FOR FURTHER INFORMATION, SEE GENERAL FLOOR REQUIREMENTS IN INSTALLATION MANUAL.

LMF-12

C-SIZE

NOTICE OF CONFIDENTIAL INFORMATION

INFORMATION CONTAINED HEREIN IS CONFIDENTIAL AND PROPERTY OF MOHAWK RESOURCES LTD., WHERE DRAWING IS FURNISHED TO OTHERS IT SHALL BE USED SOLELY FOR PURPOSES OF INSPECTION, INSTALLATION, OR MAINTENANCE. THE INFORMATION SHALL NOT BE USED OR DISCLOSED BY THE RECIPIENT FOR ANY OTHER PURPOSES WHATSOEVER.

NOTES:
1. REMOVE ALL SHARP CORNERS & EDGES.
2. UNLESS OTHERWISE SPECIFIED, SURFACE FINISH TO BE 125 RMS.
3. WELDING MEDIUM SHALL CONFORM TO AWS SPECIFICATIONS TO E-70XX ELECTRODES OR E-70T1 CODE 5.3 FLUX CORE WIRE ONLY.

TOLERANCES:
ANGULAR ± 1°
FRACTIONAL ± .030
DECIMAL:
0.XX ± .030
0.XXX ± .005

FILE NAME D12037

012-011-003
NEXT ASSEMBLY

SCALE	DRAWN	MOHAWK LIFTS, LLC.
5/64	dak	
CHECKED RW	APPROVED	TITLE: SUGGESTED IN-GROUND HYD. LINES
DATE 10/1	WEIGHT LB.	FROM / DRAWING NUMBER 012-012-037 (A)